



UPPER HALF OF
BOTTOM HALF BACK WALL
1 NEEDED

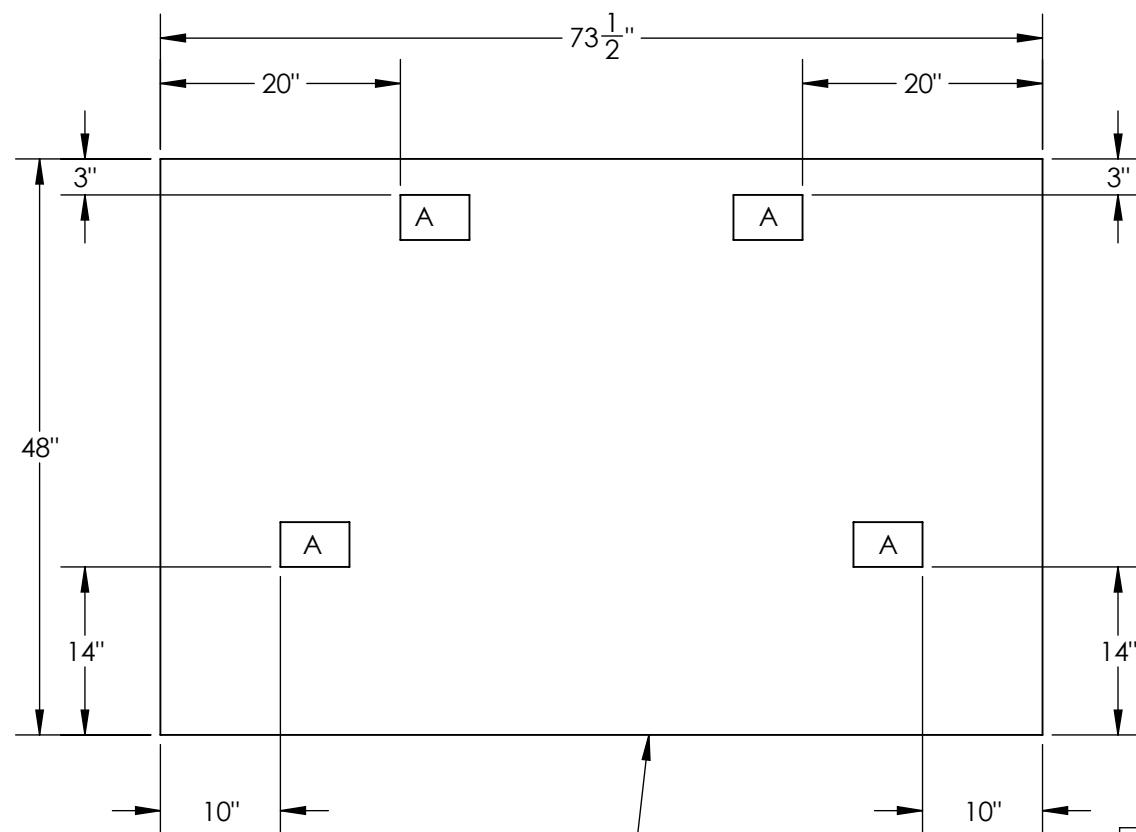

LOWER HALF OF
BOTTOM HALF BACK WALL
1 NEEDED

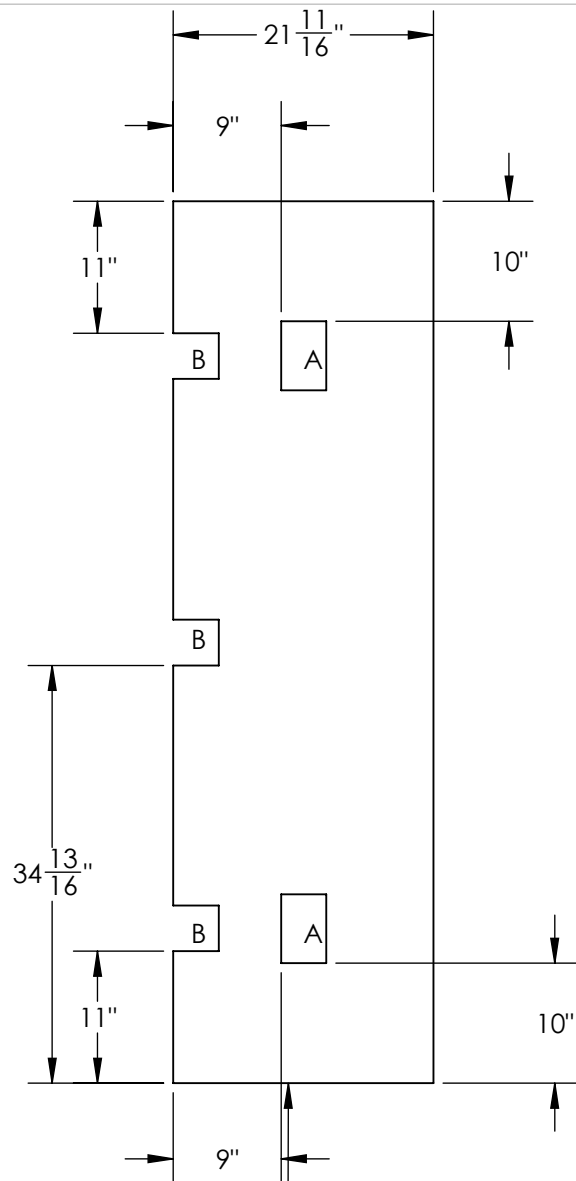

TOP HALF BACK WALL
1 NEEDED

A: 5 3/4" W x 3 3/4" L
B: 3 13/16" W x 3 13/16" L

DRAWN BY: SHELTON ADAMS


DATE: 1/28/2025

PART NAME: FINAL PIECES - BACK WALLS

UNITS: IN


PART MATERIAL: LAMINATED BIRCH PLYWOOD

SCALE: 1:16

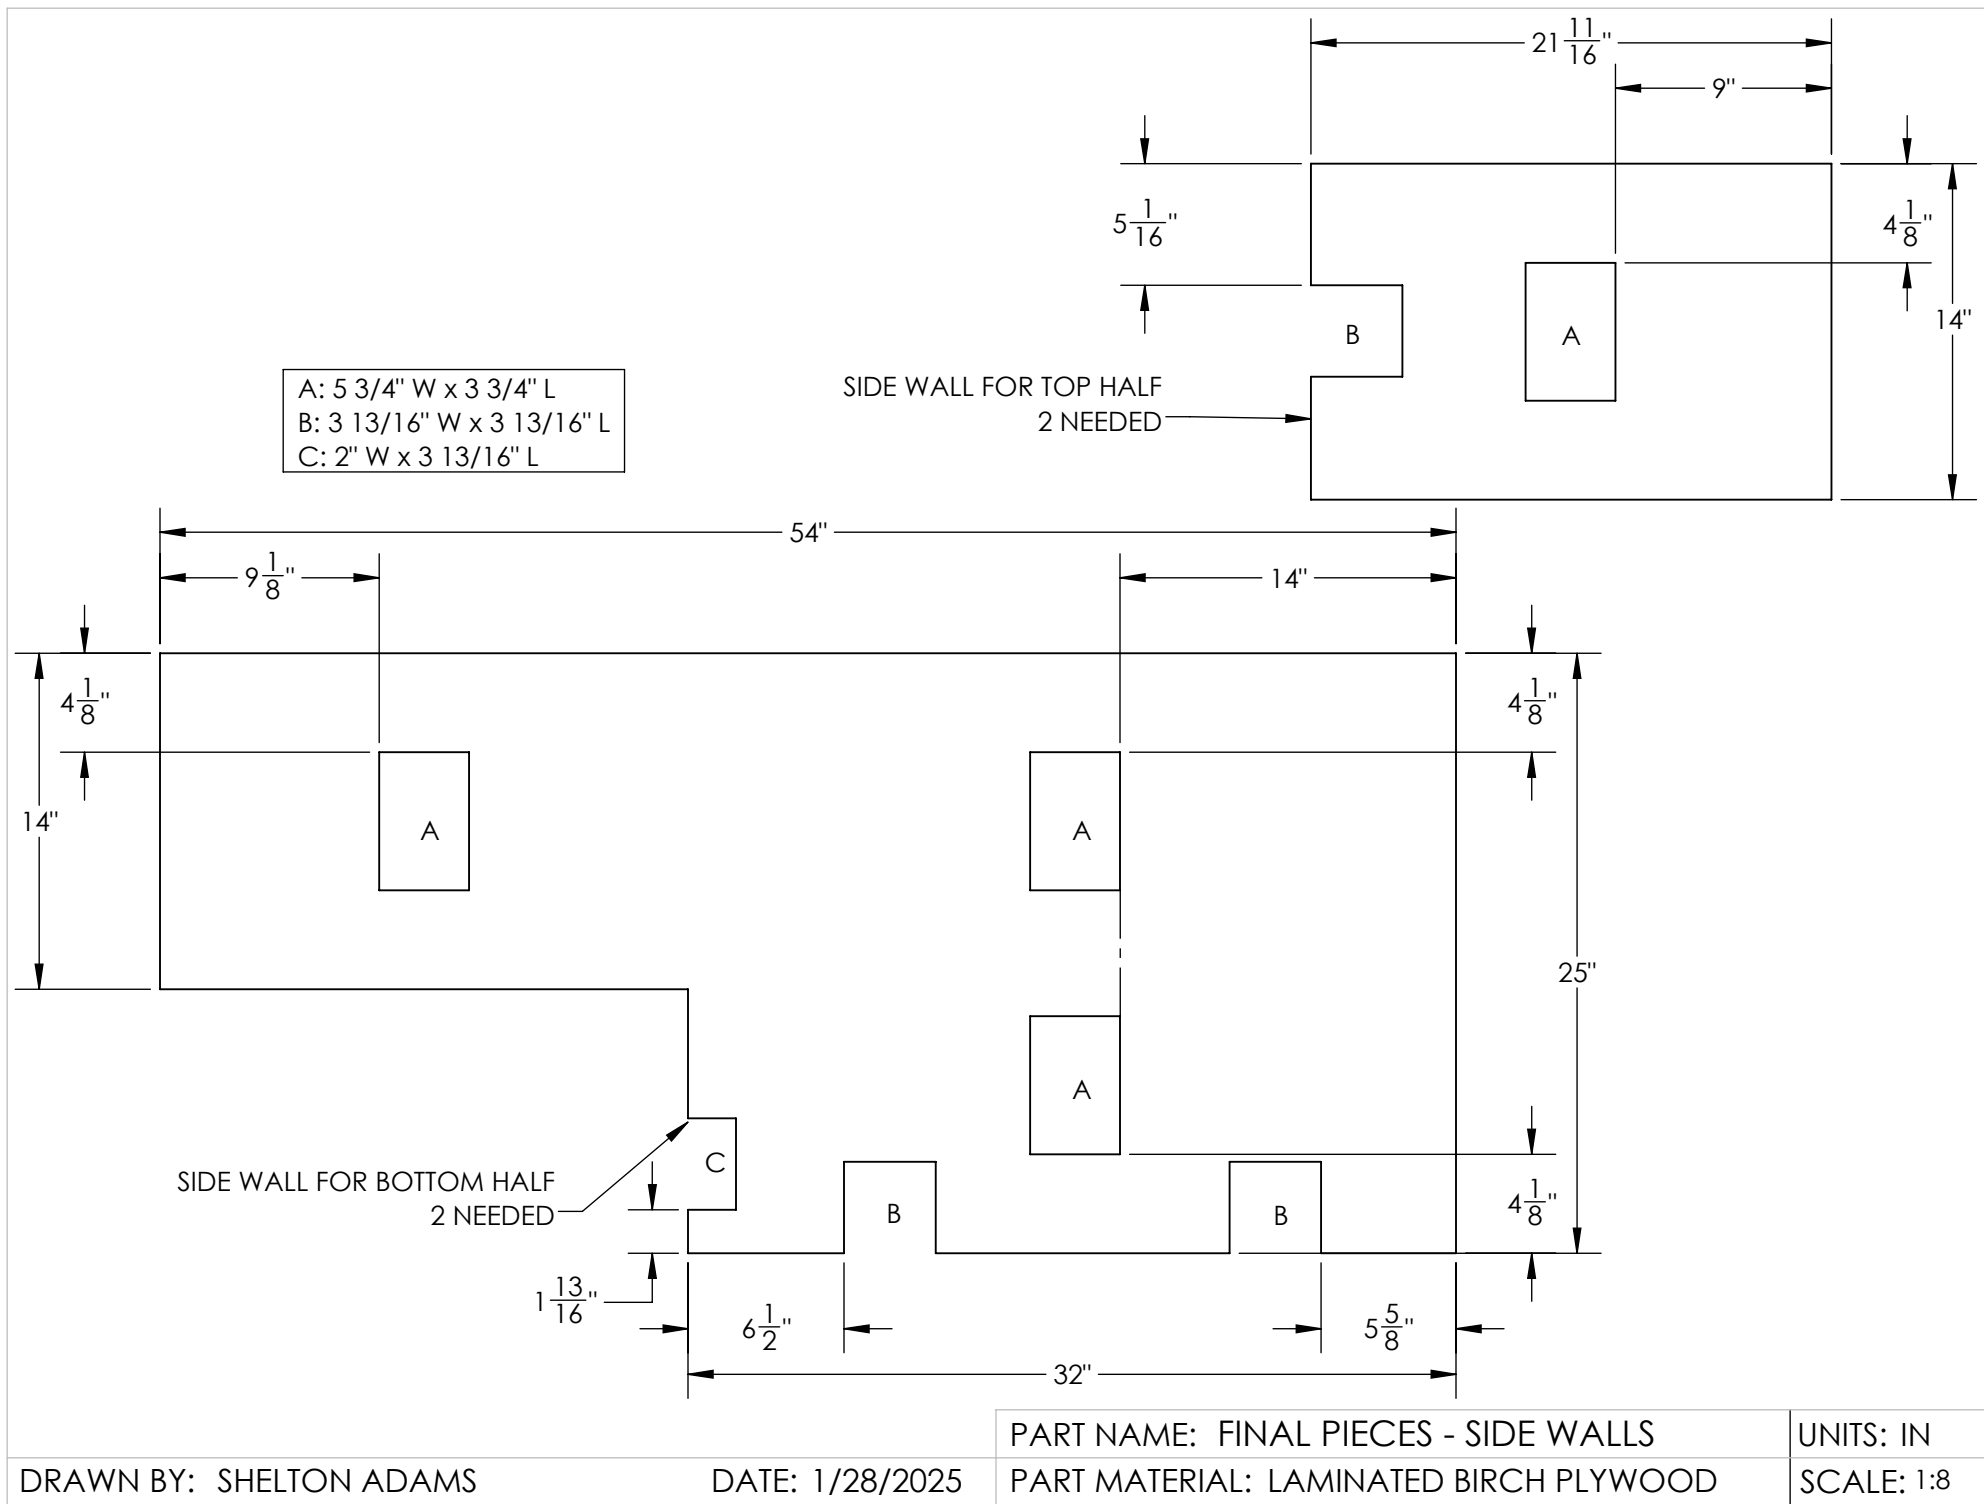

DRAWN BY: SHELTON ADAMS

DATE: 1/28/2025

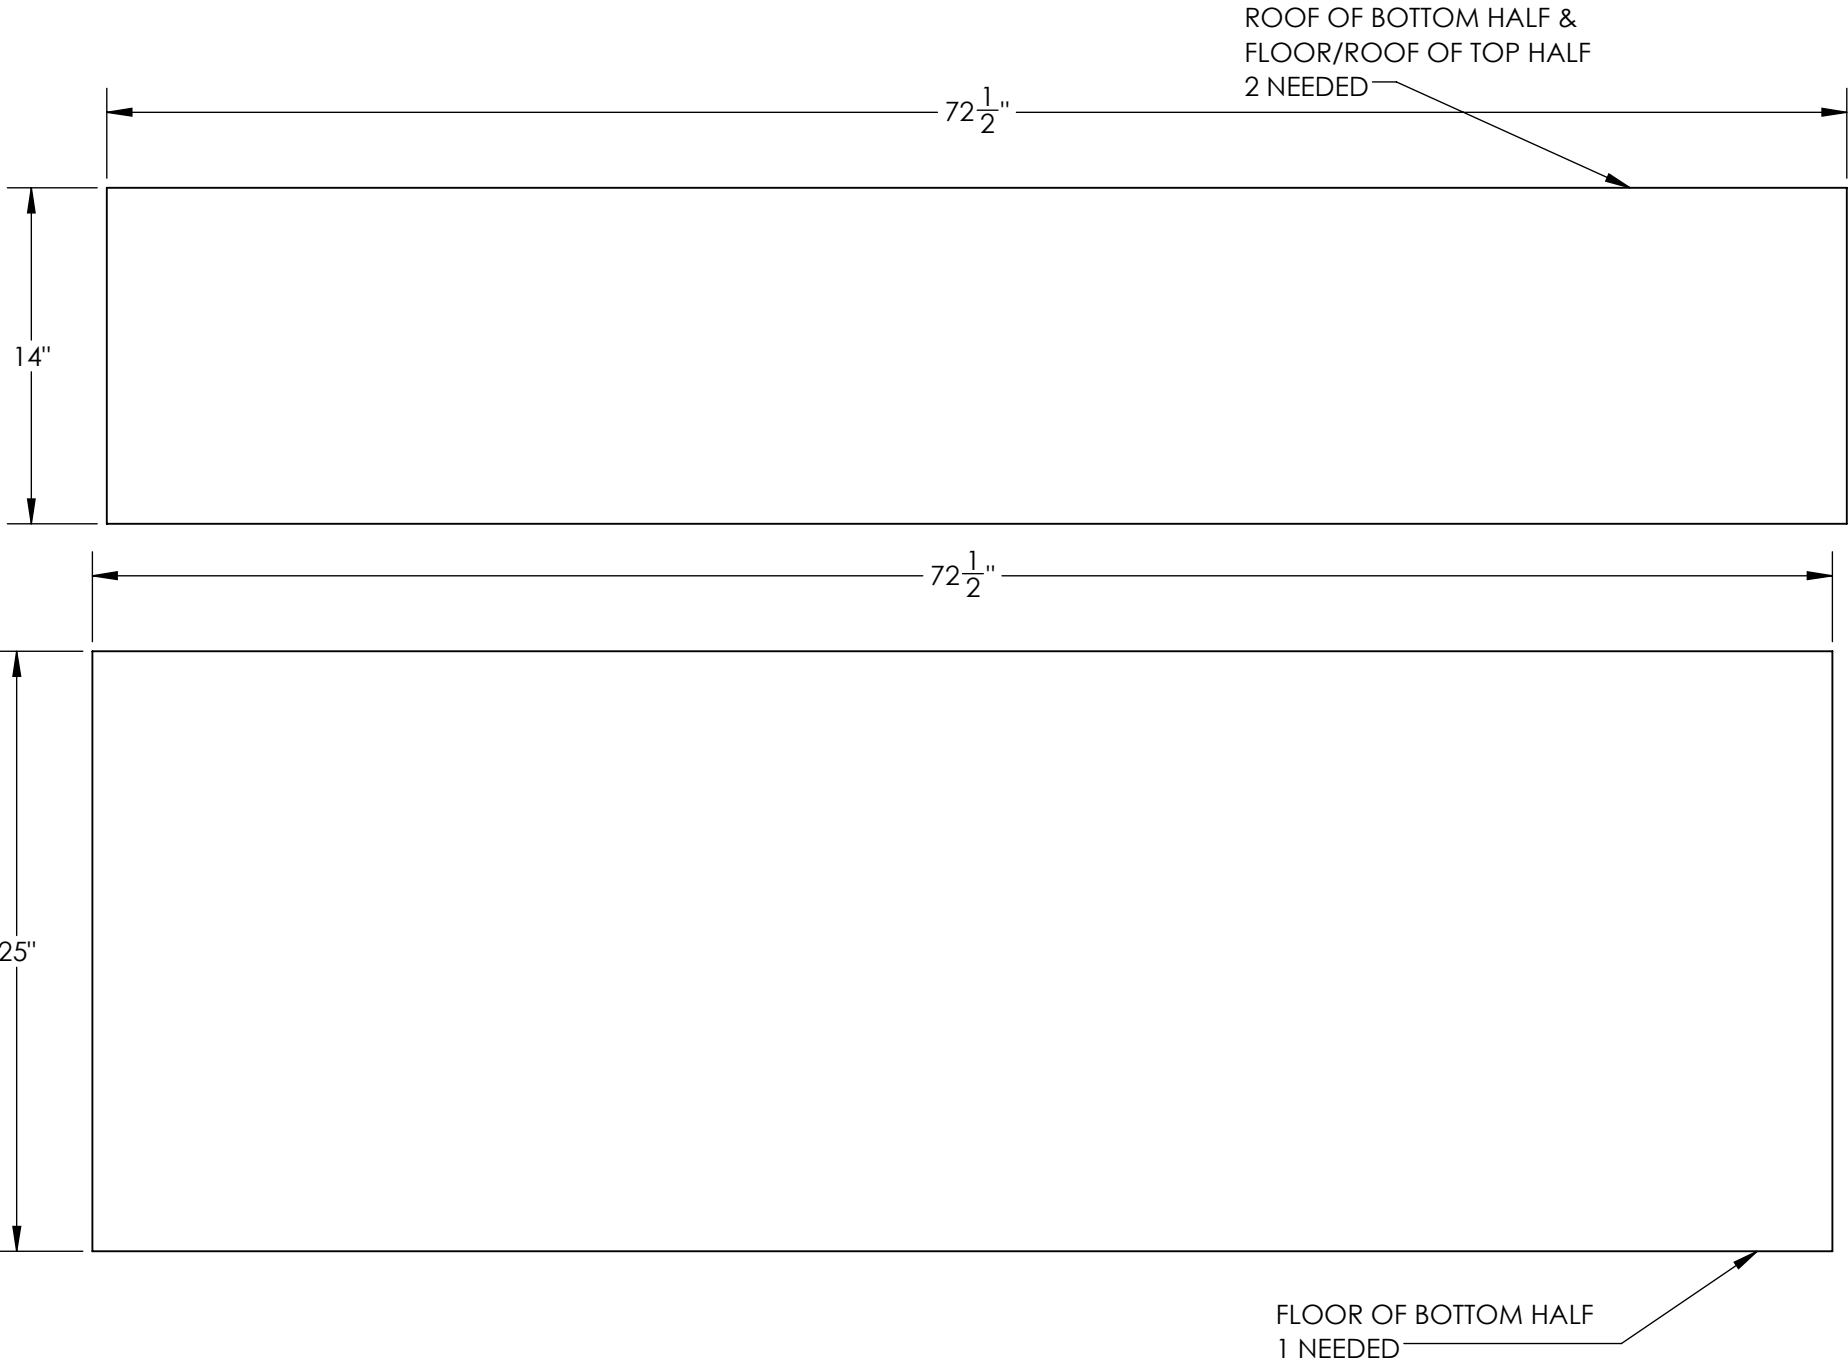

DRAWN BY: SHELTON ADAMS


DATE: 1/28/2025

PART NAME: FINAL PIECES - FLOORS & ROOFS


UNITS: IN

PART MATERIAL: LAMINATED BIRCH PLYWOOD


SCALE: 1:8

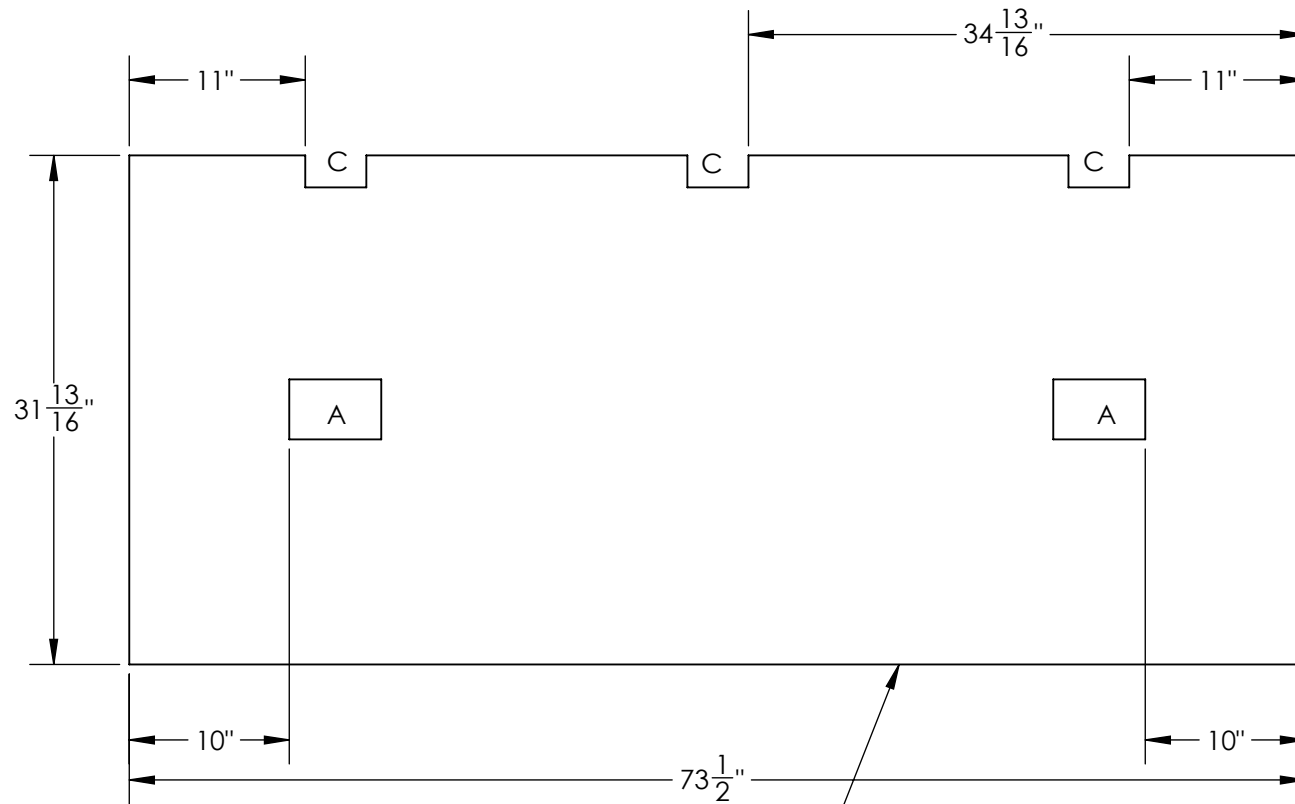

MAIN FRONT COVER PIECE
1 NEEDED

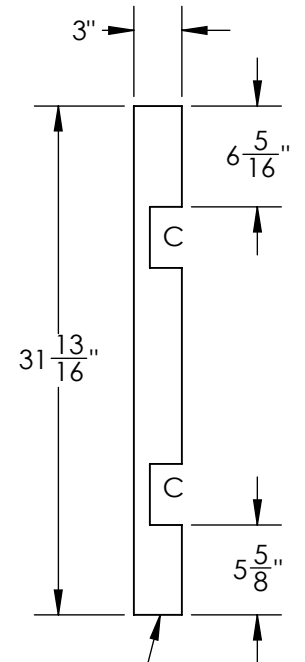

SHORT FRONT COVER SIDE PIECE
2 NEEDED

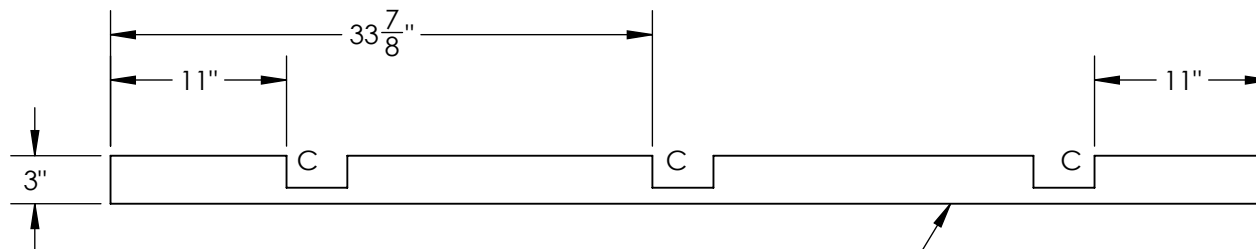

LONG FRONT COVER SIDE PIECE
1 NEEDED

A: $5\frac{3}{4}"$ W x $3\frac{3}{4}"$ L
C: 2" W x $3\frac{13}{16}"$ L

DRAWN BY: SHELTON ADAMS


DATE: 1/28/2025

PART NAME: FINAL PIECES - FRONT COVER

UNITS: IN

PART MATERIAL: LAMINATED BIRCH PLYWOOD

SCALE: 1:12

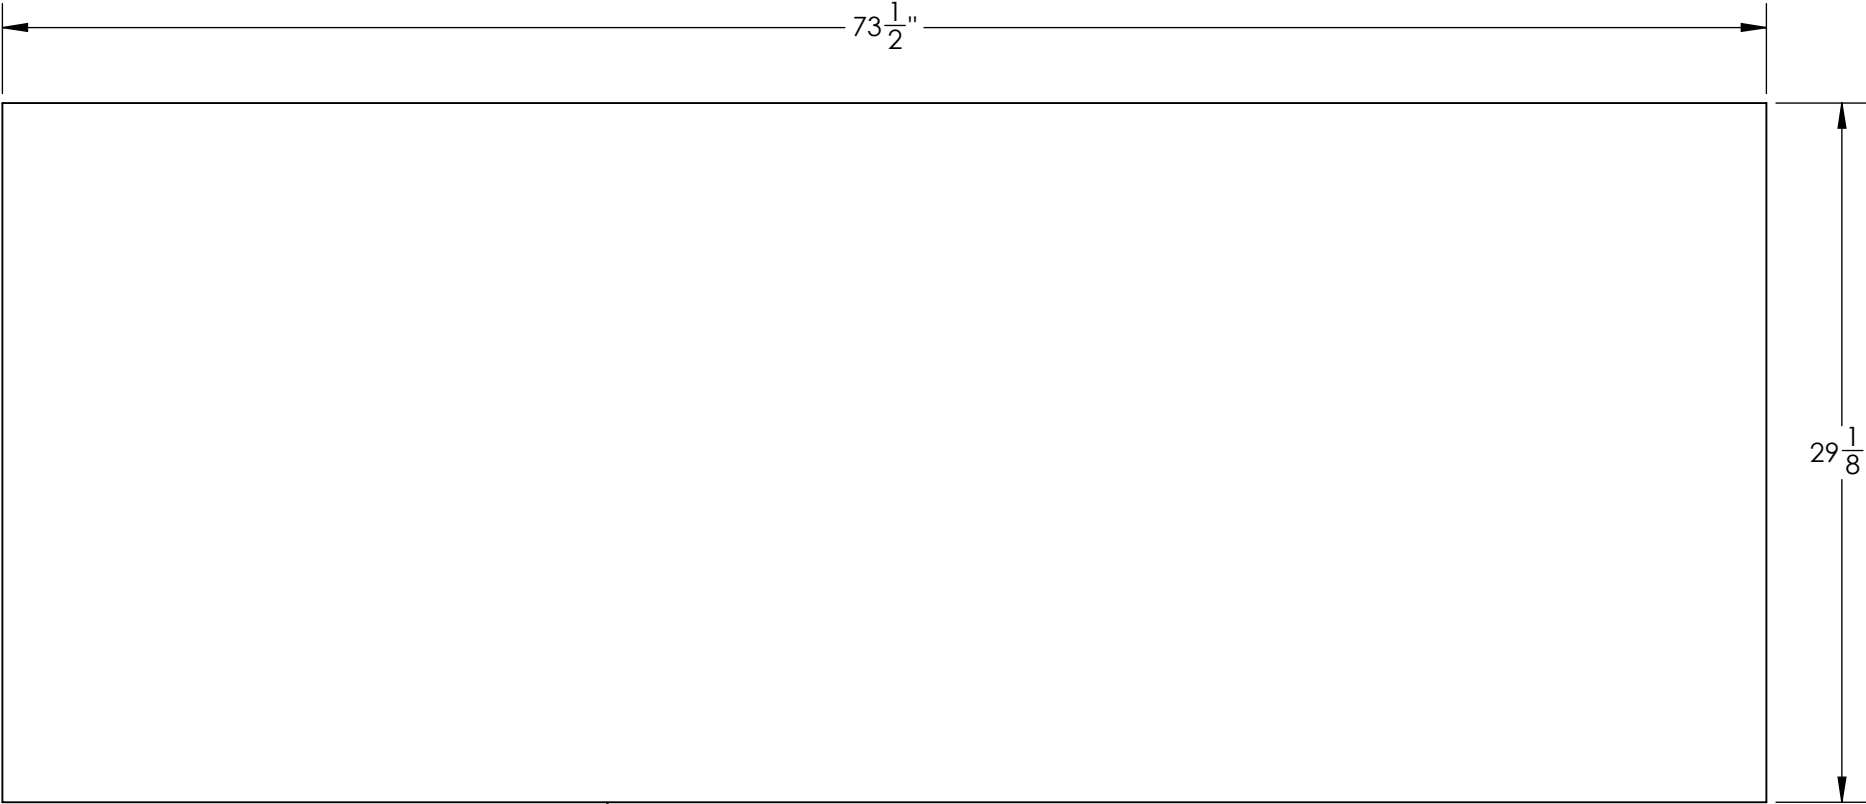

CART THING
1 NEEDED

DRAWN BY: SHELTON ADAMS

DATE: 1/28/2025

PART NAME: FINAL PIECES - CART THING

UNITS: IN

PART MATERIAL: LAMINATED BIRCH PLYWOOD

SCALE: 1:8